| TECHNOSYS INTEGRATED SOLUTIONS | SOLUTIONS FOR SAFE & SMART CITY | TECHNOSYS INTEGRATED SOLUTIONS | SOLUTIONS FOR SAFE & SMART CITY | TECHNOSYS INTEGRATED SOLU|

CITY- BILASPUR | PATCH NAME- FROM THAKUR FAMILY DHABA TO UNDER BRIDGE JALI MOR | LOCATION TYPE: SVDS

LOCATION NAME- JALI MOD

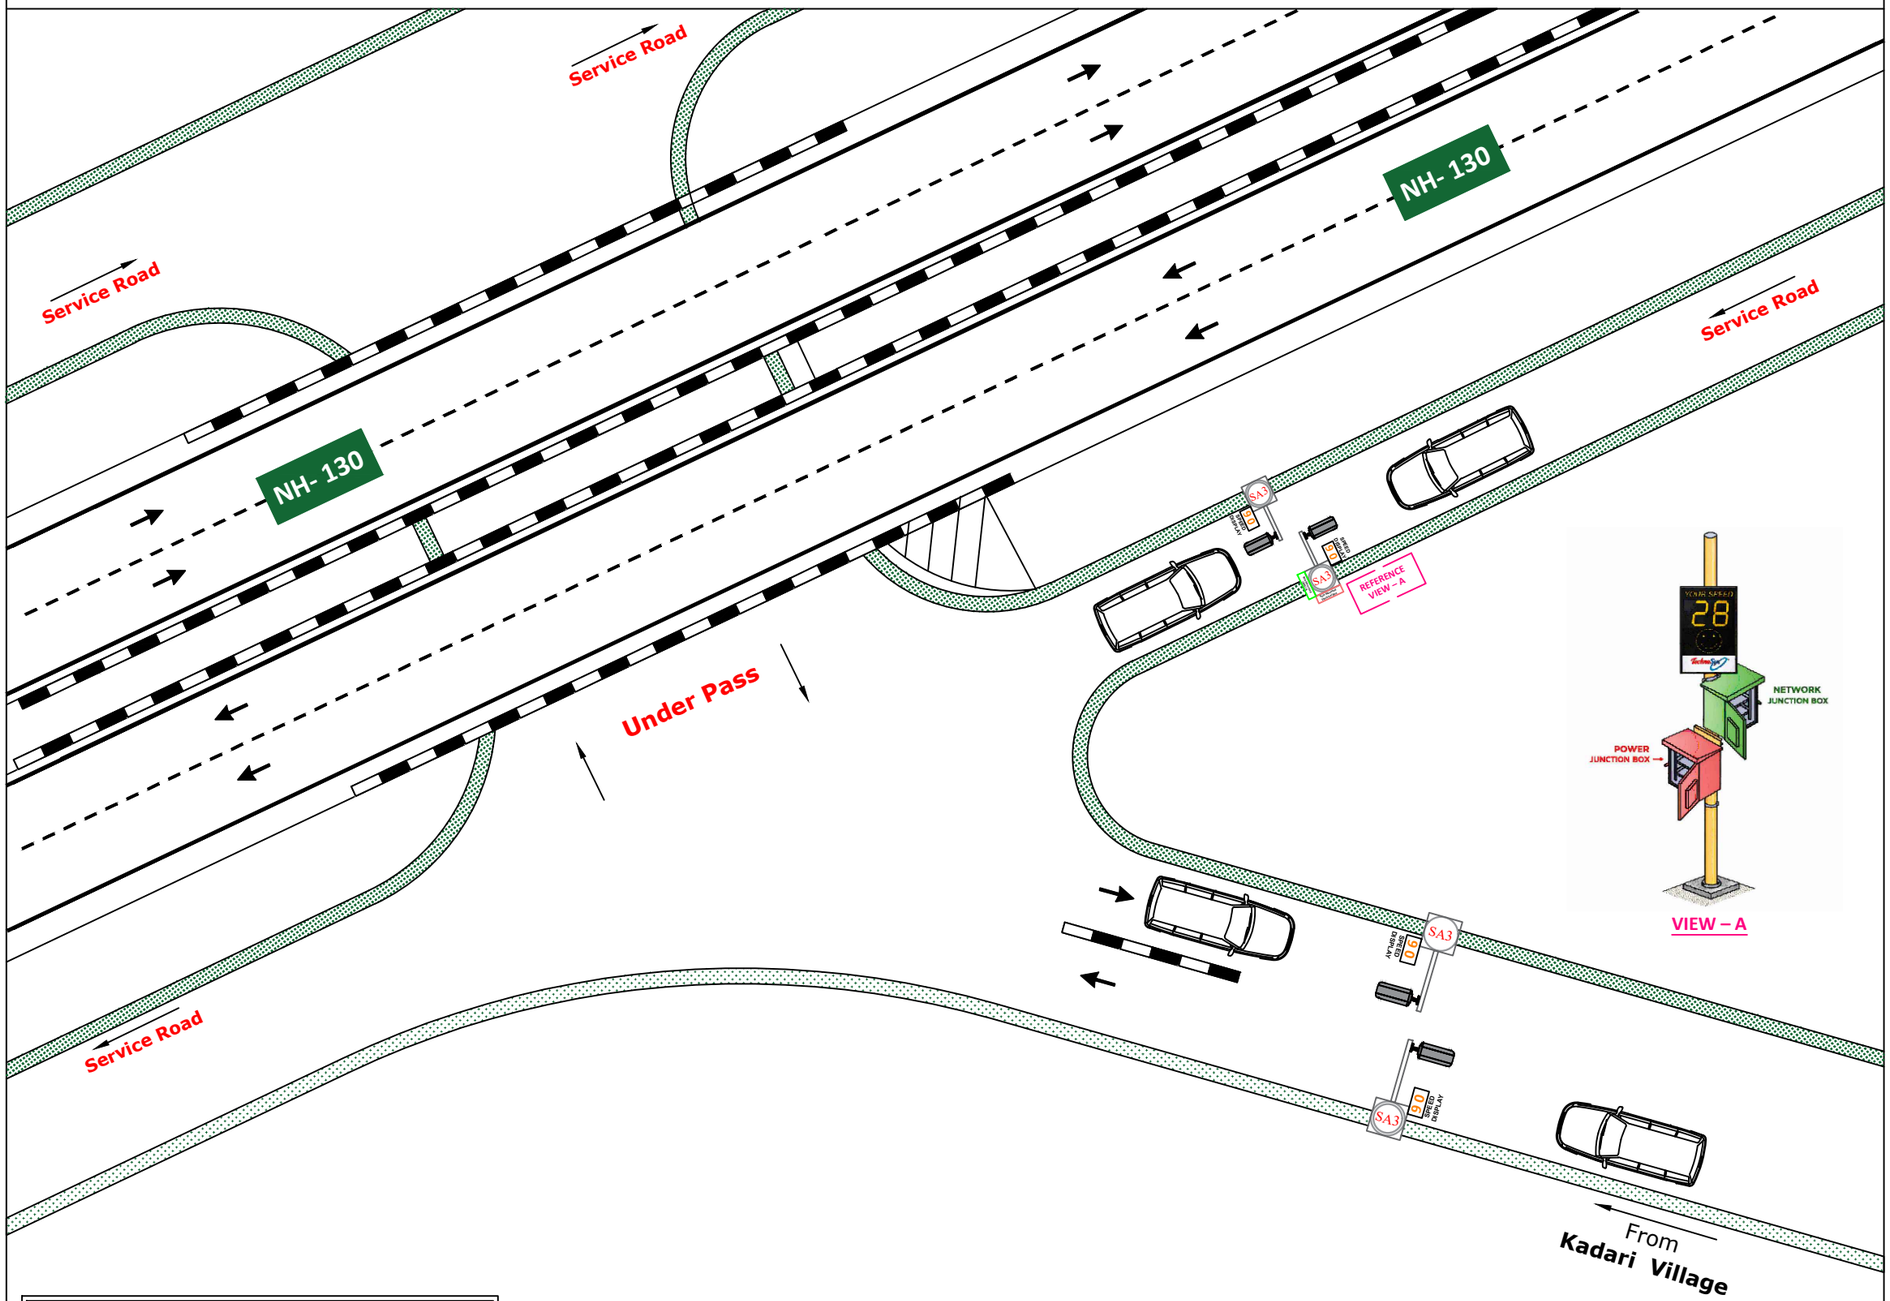

LAT LONG: 22.272068 82.2544114

LEGEND	ITEM	QTY.
	ANPR CAMERA	04
	EVIDENCE CAMERA	00
	PTZ CAMERA	00
	ELECTRICAL JUNCTION BOX	01
	NETWORK JUNCTION BOX	01
	2KVA UPS	01
VMD	VMD DISPLAY	00
R	RADAR	00
90 SPEED DISPLAY	SPEED DISPLAY	04
	PA SPEAKER	00
SP7	7 MTR. STRAIGHT POLE	00
DA3	3 MTR. DOUBLE ARM POLE	00
DA6	6 MTR. DOUBLE ARM POLE	00
DA8	8 MTR. DOUBLE ARM POLE	00
SA3	3 MTR. SINGLE ARM POLE	04
SA6	6 MTR. SINGLE ARM POLE	00
SA8	8 MTR. SINGLE ARM POLE	00
S-G	SERVICEABLE GANTRY	00
	CAT-6 CABLE	As Per Required
	POWER CABLE	As Per Required
	FOC CABLE	As Per Required
	EARTHING	05
	POLE GROUNDING	04

NOTE:
At road junction / intersection locations, the proposed pole shall be mounted on the selected approach road at a minimum distance of 20–25 meters from the road crossing end.

TechnoSys® Solutions For Safe & Smart Cities Since 2006

MSI :
TECHNOSYS INTEGRATED SOLUTIONS PVT. LTD.
E5/A, First Floor, Girish Kunj, Arera Colony, Bhopal, MADHYA PRADESH - 462016
Corporate Office: 0120-4165216
Branch Office: 0755-4201019
Website: technosysgroups.com

CLIENT:
CHHATTISGARH TRANSPORT DEPARTMENT
Office of Transport Commissioner Indravati Bhavan, 3rd Floor, C Block, Nava Raipur Chhattisgarh (CG).
Tel: 0771-2582088, 2582799
Email ID: atc.cg@gov.in
Website: cgtransport.gov.in

PROJECT: - **SITC & ELECTRONIC ENFORCEMENT OF ROAD SAFETY (CG.)**

TITLE: **JUNCTION LAYOUT**

DRAWN:	P.V	DATE:	27/01/2026	DRAWING NO: TISPL-CTD-JL-DRG-25
CHECKED	K.M	DATE:	27/01/2026	
APPROVED	H.B	DATE:	27/01/2026	

Sheet size : A3

REV: 0

| TECHNOSYS INTEGRATED SOLUTIONS | SOLUTIONS FOR SAFE & SMART CITY | TECHNOSYS INTEGRATED SOLUTIONS | SOLUTIONS FOR SAFE & SMART CITY | TECHNOSYS INTEGRATED SOLU|